

Architect

Adolph S. Rosekrans, Inc.  
950 Runnymede Road  
Woodside, CA 94062  
650.851.7201  
Fax 650.851.7202  
rosekrans@pacbell.net

**JOB COPY**

**TO REMAIN ON  
SITE AT ALL TIMES**

**SCHEDULES**

**APPROVED FOR ISSUANCE**  
This review does not authorize violation  
of State or County building laws.

Apr 10 2024

By: jbnadez

on behalf of

MATEO CO. BLDG. INSP. DIV.

**TAUBE FAMILY CARRIAGE HOUSE  
San Mateo County History Museum  
MUSEUM ADDITION**  
San Mateo County Historical Association  
2200 Broadway Redwood City, CA 94063

Date 12-20-2022

Scale U.O.N.

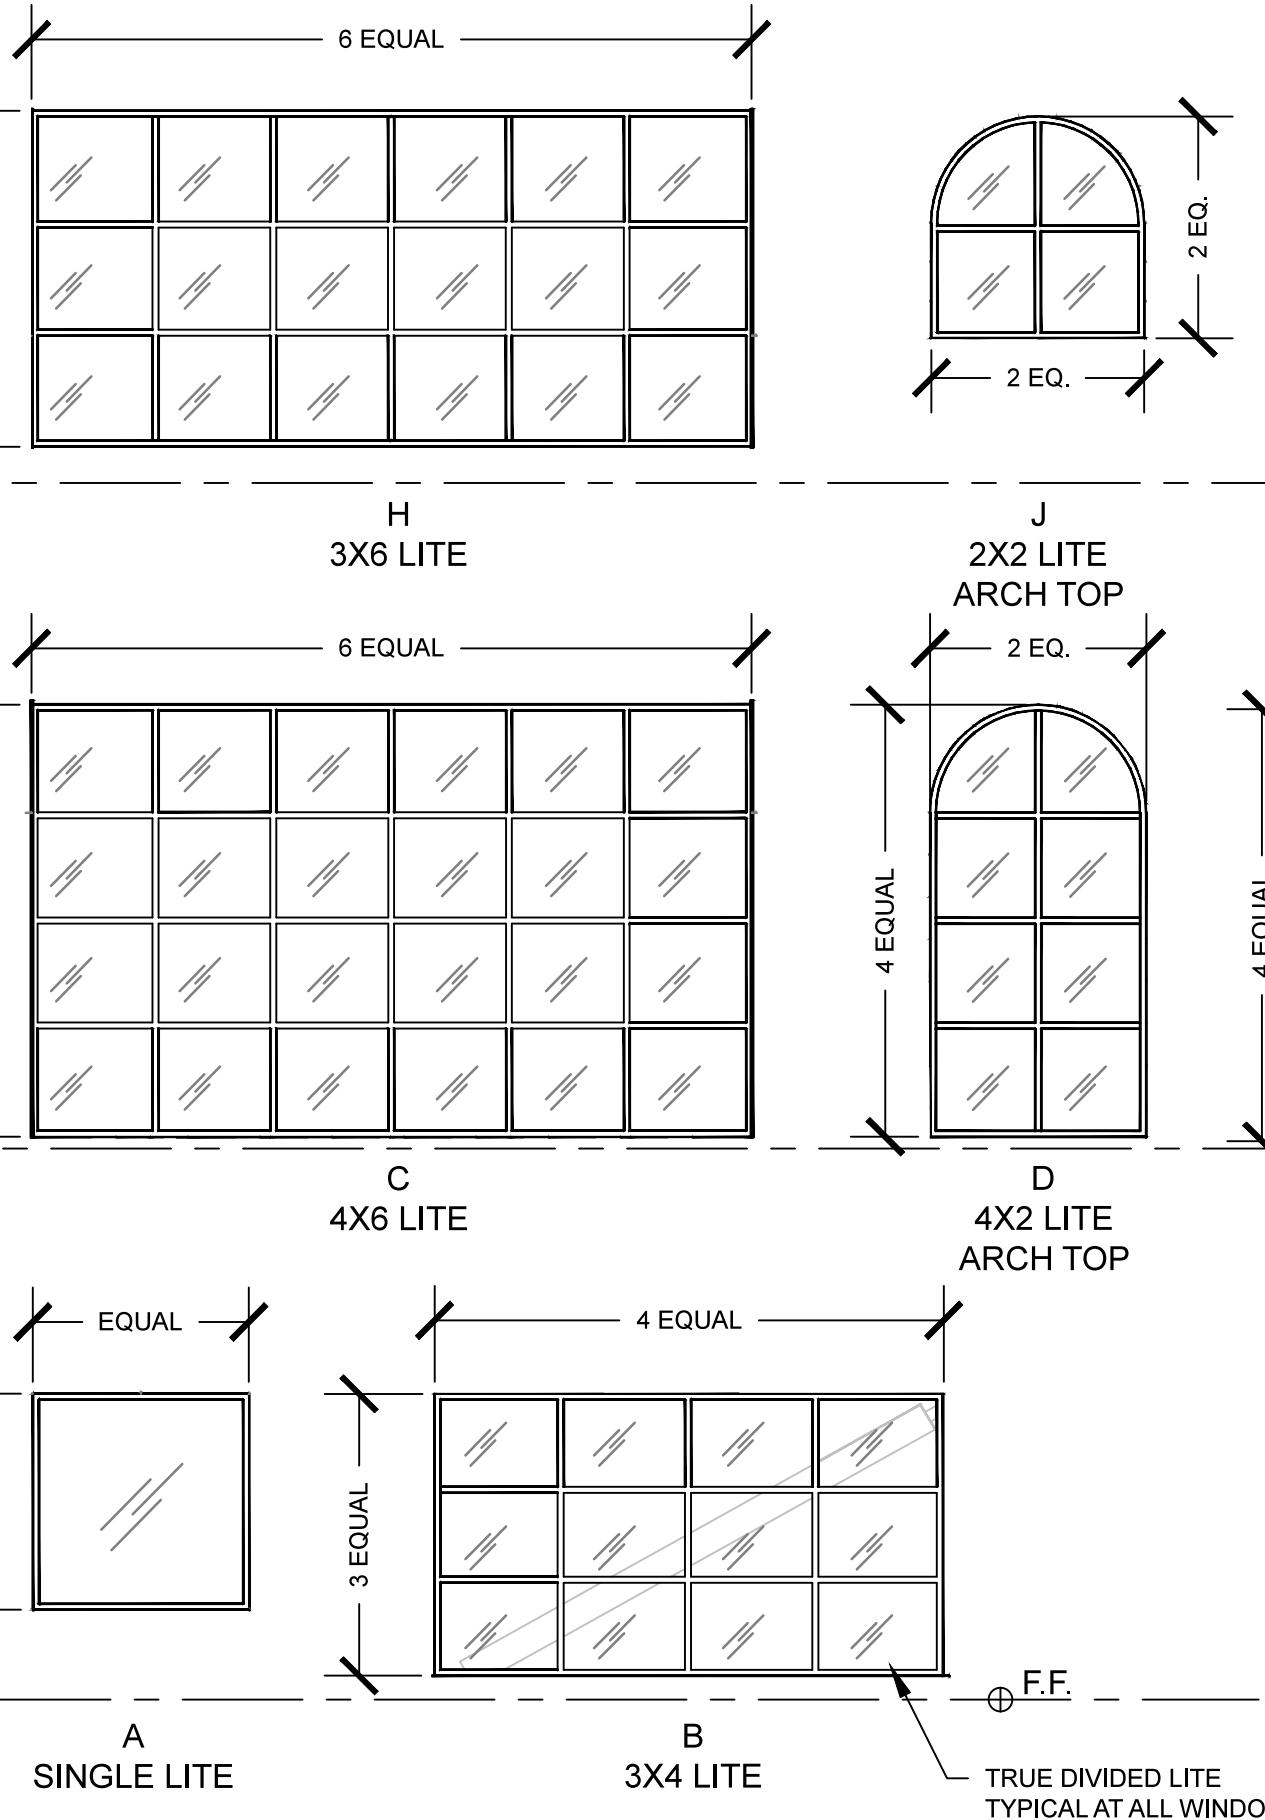
Job 1702

**G1.1**

Sheet

**WINDOW SCHEDULE**

MARK	TYPE	W X H	GLAZING		SHADE	FINISH	NOTE	COMMENTS
			U-FACT	SHGC				
<b>GROUND FLOOR</b>								
101		6'-0" X 6'-0"	0.44	0.20				
102		6'-0" X 6'-0"	0.44	0.20				
103	A	6'-0" X 6'-0"	0.44	0.20	10%	KYNAR	5	
104		6'-0" X 6'-0"	0.44	0.20				
105		6'-0" X 6'-0"	0.44	0.20				
106	B	14'-2" X 8'-6"	0.44	0.20	5%	KYNAR	3.5	
107	K	12'-8" X 8'-6"	0.44	0.20	5%	KYNAR	3.5	
<b>FIRST FLOOR</b>								
201	C	20'-0" X 12'-0"	0.44	0.20	5%	KYNAR	3.5	
202	D	6'-0" X 12'-0"	0.44	0.20	N/A	KYNAR	3	ARCH TOP
203		6'-0" X 12'-0"	0.44	0.20	5%	KYNAR	3.5	ARCH TOP
204								
205								
206	G	9'-4" X 12'-0" EACH	0.44	0.20	5%	KYNAR	3.5	
207								
208								
209								
210								
211	D	6'-0" X 12'-0"	0.44	0.20	5%	KYNAR	3.5	ARCH TOP
212	D	6'-0" X 12'-0"	0.44	0.20	N/A	KYNAR	3	ARCH TOP
213	F	6'-0" X 6'-0"	0.44	0.20	N/A	KYNAR		
214	E	14'-2" X 12'-0"	0.44	0.20	5%	KYNAR	3.5	
215	G	12'-8" X 12'-0"	0.44	0.20	5%	KYNAR	3.5	
<b>SECOND FLOOR</b>								
301								
302								
303	K	9'-4" X 9'-4" EACH	0.44	0.20	10%	KYNAR	3.5	
304								
305								
306								
307								
308								
309								
310								
311	J	6'-0" X 6'-0"	0.44	0.20	N/A	KYNAR	3.5	ARCH TOP
312	J	6'-0" X 6'-0"	0.44	0.20	5%	KYNAR	5	ARCH TOP
313	J	6'-0" X 6'-0"	0.44	0.20	5%	KYNAR	5	ARCH TOP
314	J	6'-0" X 6'-0"	0.44	0.20	N/A	KYNAR		ARCH TOP
<b>NOTES</b>								
1	ALL WINDOWS INCLUDING SHALL BE NFRC CERTIFIED							
2	ALL WINDOWS TO BE METAL WITH DOUBLE PANE WITH THERMAL BREAK FRAMES & NFRC CERTIFIED WITH OVERALL VT = .41 MAX. TRUE DIVIDED LITES.							
3	PROVIDE SAFETY GLASS AT ALL HAZARDOUS LOCATIONS AS LISTED IN CBC 2406 INCLUDING BUT NOT LIMITED TO: PANES >9 S.F.; BOTTOM EDGE <18" A.F.F.; DOORS & SIDELITES							
4	NOT USED							
5	SHADE SPEC: ROLLER SHADE AT EACH WINDOW NOTED. ALL TO INCLUDE AUTO-OPERATION TIED TO LIGHTING CONTROLS.							

**WINDOW SCHEDULE AND NOTES****WINDOW TYPES**TRUE DIVIDED LITE  
TYPICAL AT ALL WINDOWS**DOOR SCHEDULE**

MARK	TYPE	W X H	MATERIAL		FRAME	FINISH	HDWR	COMMENT
			FINISH	OPEN				
<b>GROUND FLOOR</b>								
101	D	6'-0" X 8'-0"	0.44	0.20				
102	D	6'-4" X 8'-0"	0.44	0.20				
103	D	6'-4" X 7'-0"	0.44	0.20	10%	KYNAR	5	
104	CO	6'-6" X 7'-0"	0.44	0.20	N/A	GB		PAINT
105	ELEV	3'-6" X 7'-0"	0.44	0.20	MTL	MTL	BAKED ENAMEL	15 PER MANUFACTURER
106	CO	6'-7" X 8'-0"	0.44	0.20	N/A	GB	PAINT	
107	A-V	3'-0" X 7'-0"	0.44	0.20	WOOD	MTL	PAINT	04 MEN'S RR SIGNAGE. 18X24 METAL LOUVER
108	A-V	3'-0" X 7'-0"	0.44	0.20	WOOD	MTL	PAINT	06 18X24 METAL LOUVER
109	AA	6'-0" X 7'-0"	0.44	0.20	WOOD	MTL	PAINT	13
110	A-V	3'-0" X 7'-0"	0.44	0.20	WOOD	MTL	PAINT	06 18X24 METAL LOUVER
111	A	3'-0" X 7'-0"	0.44	0.20	WOOD	MTL	PAINT	08 WOMEN'S RR SIGNAGE. 18X24 METAL LOUVER
112	A-V	3'-0" X 7'-0"	0.44	0.20	WOOD	MTL	PAINT	05 XOO SLIDER PROVIDE ROLLER SHADE; NOTE 5
113	A-V	3'-0" X 7'-0"	0.44	0.20	WOOD	MTL	PAINT	08A 60 MIN. FIRE RATED
114	A	3'-0" X 7'-0"	0.44	0.20	WOOD	MTL	PAINT	06A 60 MIN. FIRE RATED
115	B	3'-0" X 7'-0"	0.44	0.20	MTL	MTL	PAINT	01 WITH GLASS TRANSOM ABOVE
116	E	20'-0" X 8'-6"	0.44	0.20	GLASS	MTL	KYNAR	16 XOO SLIDER PROVIDE ROLLER SHADE; NOTE 5
117	A	3'-0" X 7'-0"	0.44	0.20	MTL	MTL	PAINT	02 60 MIN. FIRE RATED
118	A	3'-0" X 7'-0"	0.44	0.20	MTL	MTL	PAINT	10 60 MIN. FIRE RATED
119	AA	6'-0" X 7'-0"	0.44	0.20	WOOD	MTL	PAINT	17
120	CO	7'-8" X 8'-5"	0.44	0.20	N/A	GB	PAINT	-
121	CO	8'-1" X 8'-5"	0.44	0.20	N/A	GB	PAINT	-
122	CO	7'-8" X 8'-5"	0.44	0.20	N/A	GB	PAINT	-
<b>FIRST FLOOR</b>								
201	C	20'-0" X 12'-0"	0.44	0.20	5%	KYNAR	3.5	
202	D	6'-0" X 12'-0"	0.44	0.20	N/A	KYNAR	3	ARCH TOP
203		6'-0" X 12'-0"	0.44	0.20	5%	KYNAR	3.5	ARCH TOP
204								
205	G	9'-4" X 12'-0" EACH	0.44	0.20	10%	KYNAR	3.5	
206					</			